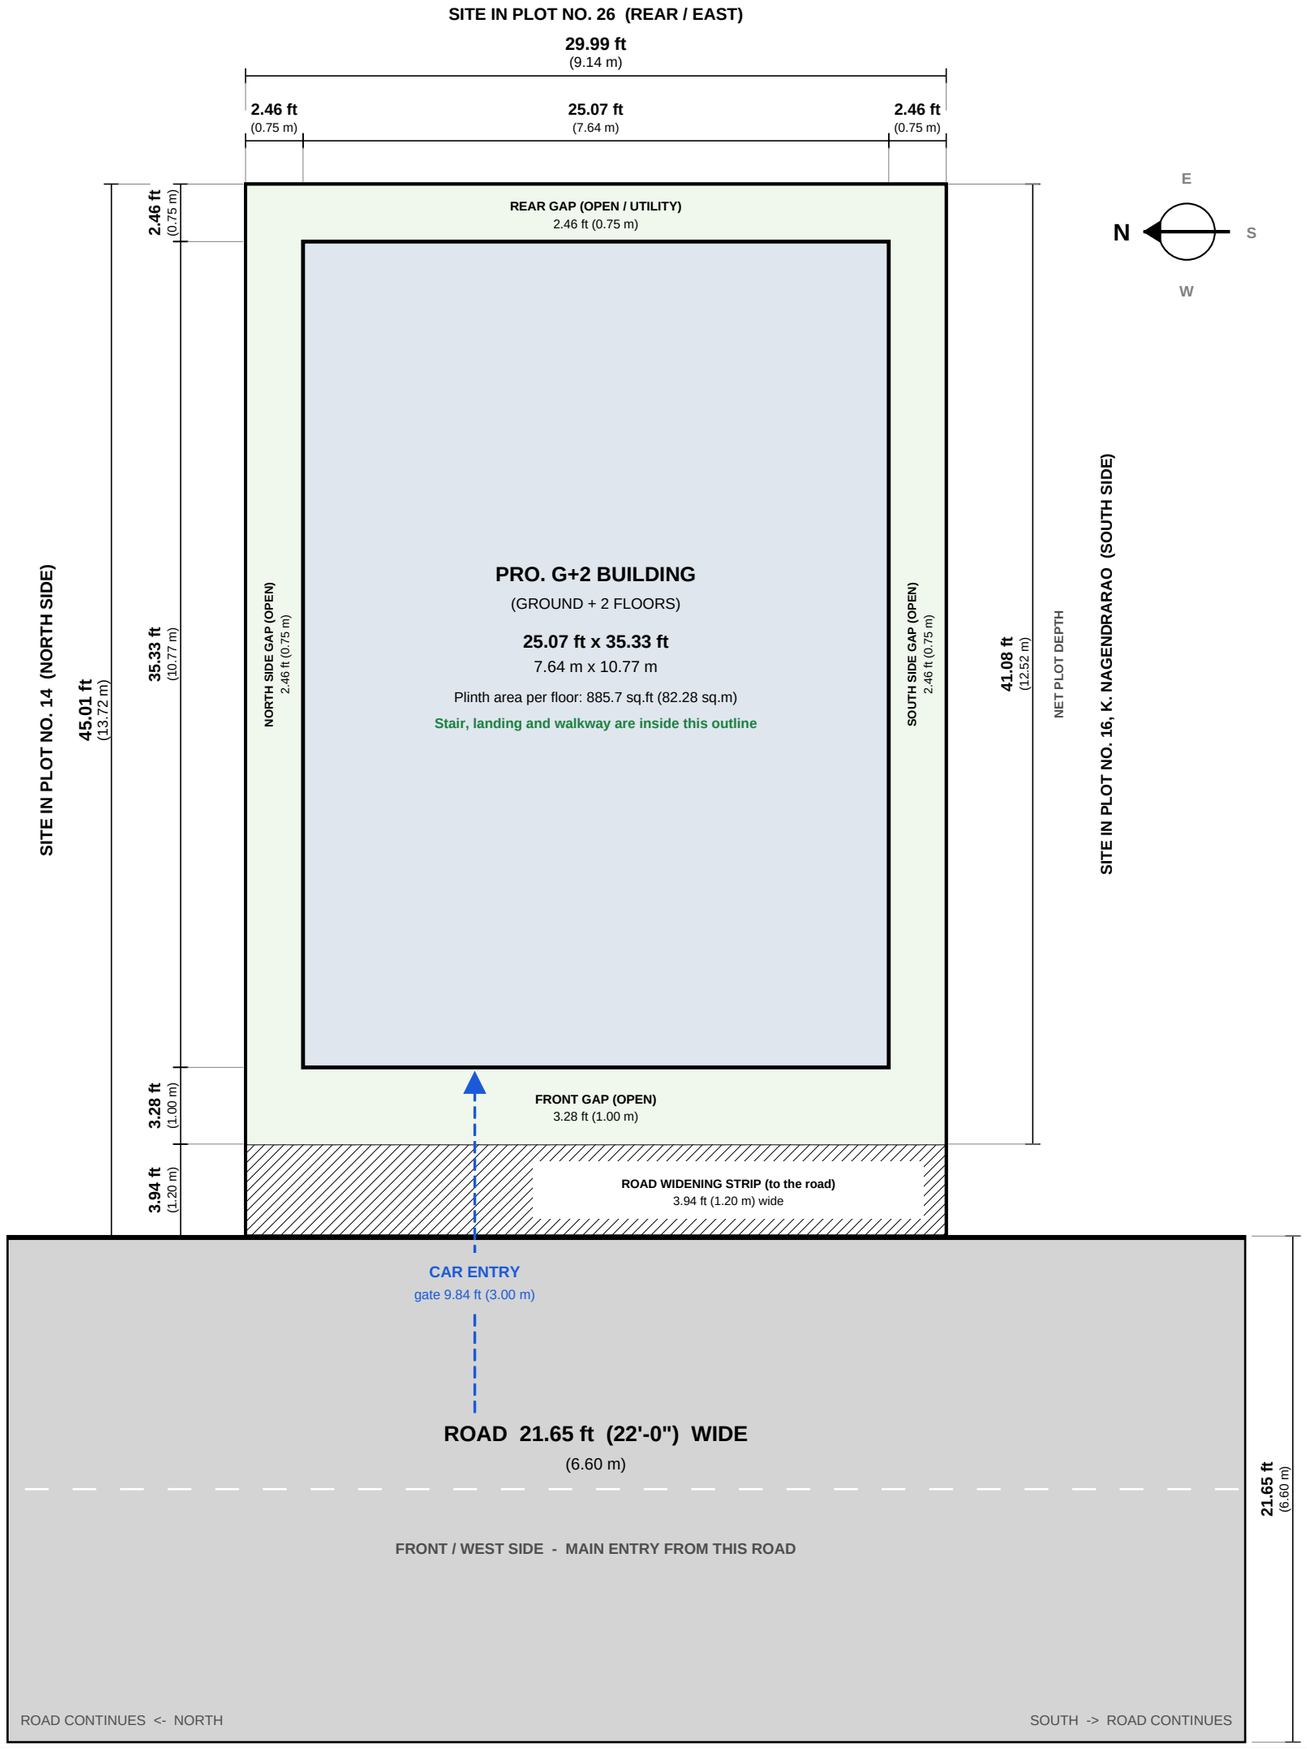

SITE PLAN

PLAN SHOWING THE PROPOSED G+2 RESIDENTIAL BUILDING IN PLOT NO. 15, KATHERUVU VILLAGE AND PANCHAYAT, RAJAMAHENDRAVARAM RURAL, E.G.DIST.

Every measurement is given in FEET (bold) with the same value in METRES (in brackets). Scale 1:80 on A3.
Orientation as in the floor plans: road (west) at the bottom, north to the left.

PLOT, BUILDING AND OPEN GAPS	FEET	METRES
Total plot, including road widening	**29.99 ft x 45.01 ft**	9.14 x 13.72 m
Road widening strip (goes to the road)	**29.99 ft x 3.94 ft**	9.14 x 1.20 m
Net plot after the road widening	**29.99 ft x 41.08 ft**	9.14 x 12.52 m
Building plinth (every floor)	**25.07 ft x 35.33 ft**	7.64 x 10.77 m
Open gap at the rear (east)	**2.46 ft**	0.75 m
Open gap on the north side	**2.46 ft**	0.75 m
Open gap on the south side	**2.46 ft**	0.75 m
Open gap at the front (west)	**3.28 ft**	1.00 m
Road in front of the plot, full width	**21.65 ft (22'-0")**	6.60 m
Car gate in the front wall	**9.84 ft**	3.00 m

AREAS	SQ.FT	SQ.M
Total site area	**1,349.9**	125.41
Road widening area	**118.0**	10.96
Net site area	**1,231.9**	114.45
Plinth area, ground floor	**885.7**	82.28
Plinth area, first floor	**885.7**	82.28
Plinth area, second floor	**885.7**	82.28
Built-up area (3 floors)	**2,657.0**	246.84
Open site area (net site - plinth)	**346.3**	32.17

WHAT THE DRAWING SHOWS

- Building outline = the plinth: 25.07 ft x 35.33 ft (7.64 m x 10.77 m). It is the same on all three floors.
- The stair, its landing and the walkway are inside this outline, so nothing projects into the open gaps or the road widening.
- The four open gaps (grey-green) are measured from the plot boundary to the building wall.
- The hatched strip at the front is the road widening: it is part of the total site area but belongs to the road.
- Blue dashed arrow: the way a car comes in from the road to the parking gate.

NOTE ON THE CONVERSION

Feet are converted exactly from the metre sizes (1 m = 3.28084 ft), so the building is 25.07 ft wide (the hand sketch shows 25 ft) and 35.33 ft deep (sketch 35.3 ft). The metre values are the approved ones.

APPLICANT SIGNATURE

LICENSED ENGINEER